

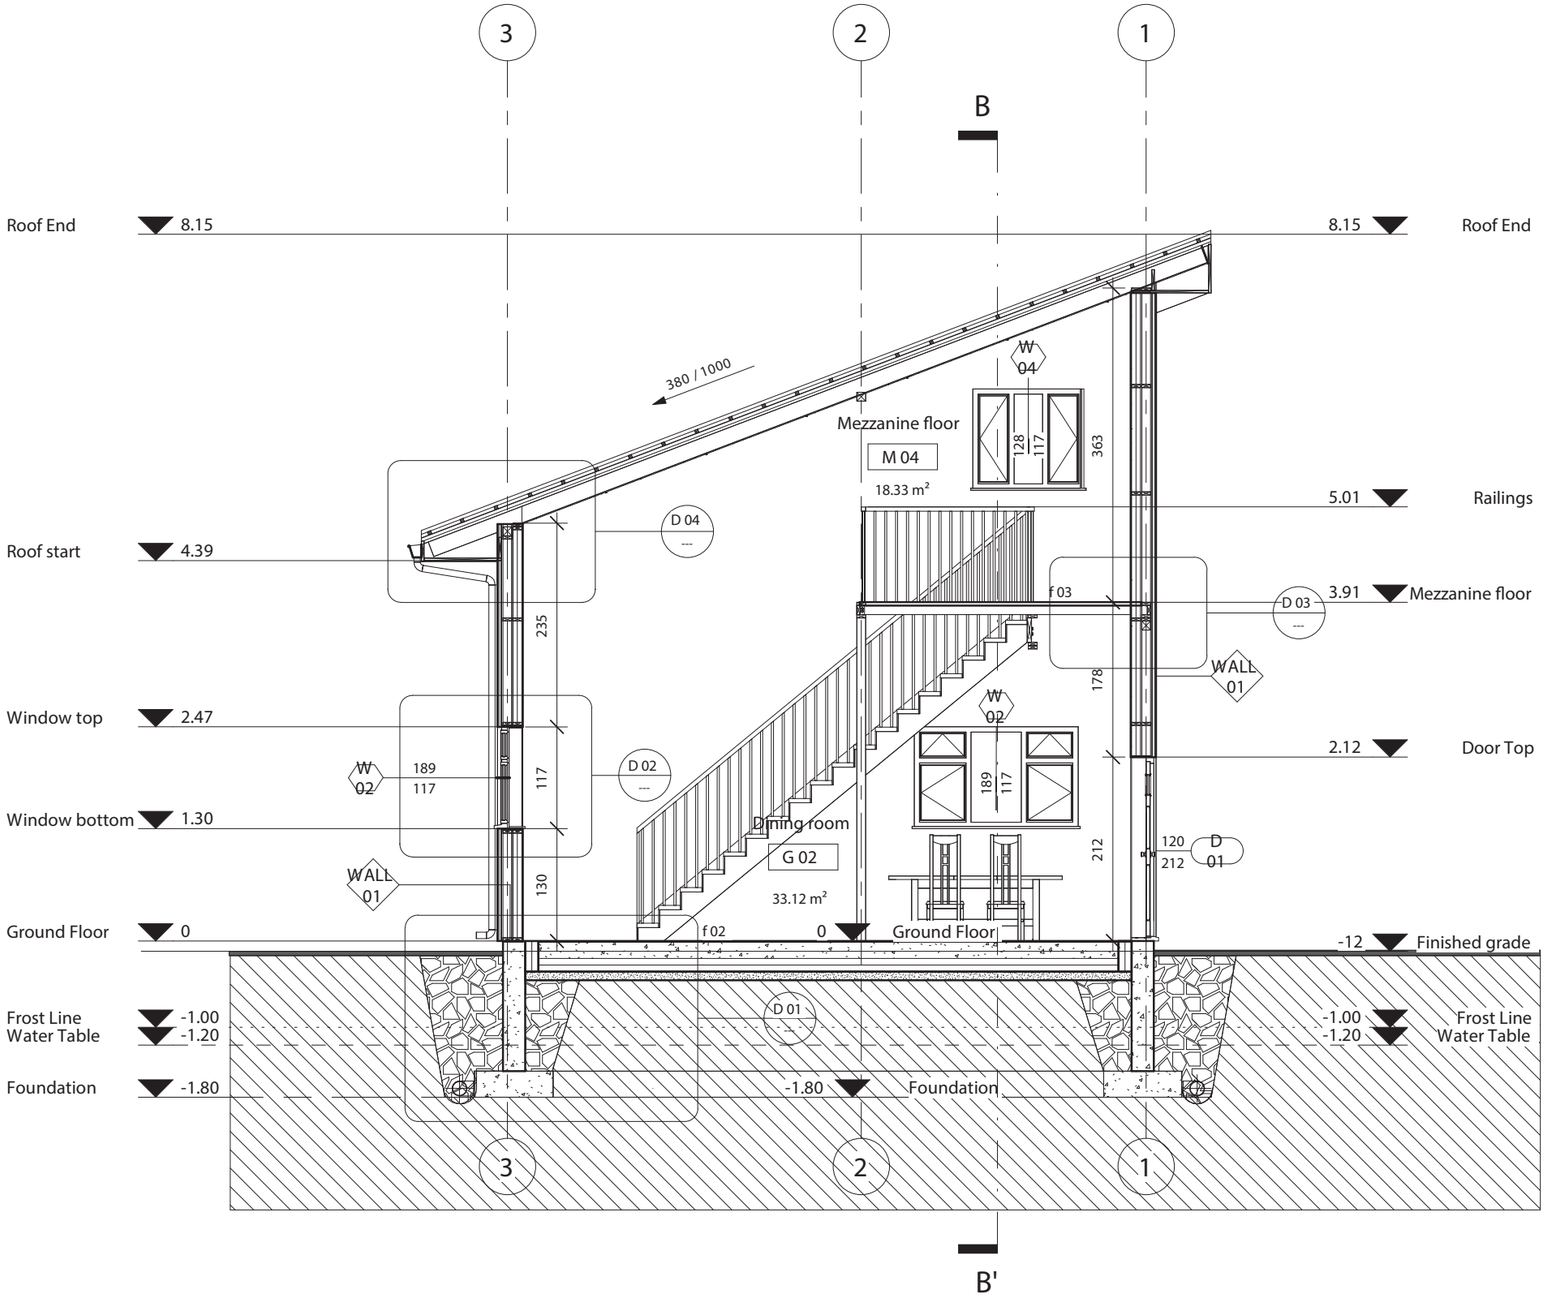


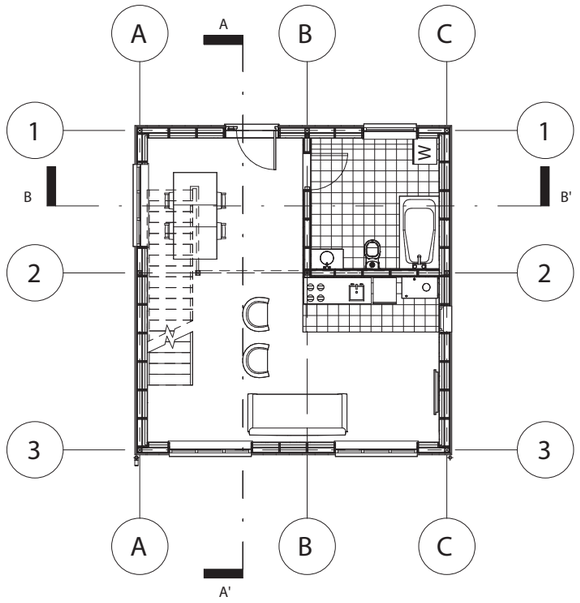

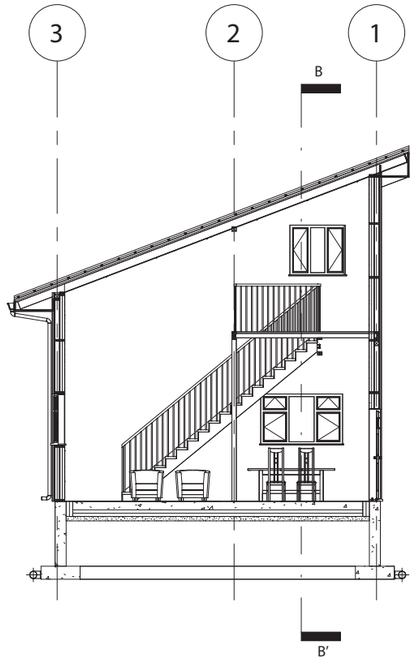

WALL 01	
Gypsum wall board	1 cm
Air	5.2 cm
Rockwool insulation	5 cm
OSB	1.5 cm
Air infiltration barrier	0.2 cm
Rockwool insulation	10 cm
OSB	1.5 cm
Breather membrane (Dupont Tyvek)	0.5 cm
Waterproofing membrane	0.1 cm
Battens	2.5 cm
Timber cladding	1.7 cm

ROOF	
Roof tile	4 cm
Horizontal and vertical battens	7.6 cm
Polyurethane breather membrane	0.5 cm
OSB panels	3 cm
Mineral wool insulation between rafters	18 cm
Damp proof membrane	0.2 cm
Gypsum board	1cm

f 02	
PVC floor finishing	0.5 cm
Cast in situ concrete slab	20 cm
Damp proof membrane	0.2 cm
XPS insulation	2x7.6 cm
Waterproofing membrane	0.1 cm
Sand blinding	10 cm
Gravel	

f 03	
PVC floor finish	0.25 cm
OSB	3.8 cm

TBM = 938

N

M.E.T.U. FACULTY OF ARCHITECTURE DEPARTMENT OF ARCHITECTURE	ARCH351	BUILDING DETAIL MODELLING
	CHECKED BY:	
PORTFOLIO SUBMISSION		SCALE: 1/50
SECTION AA'		SHEET: A3
		FINAL EXAM
DRAWING BY: CİHAN AY - CİHAT İLKBAHAR		DATE: 30.01.2022