

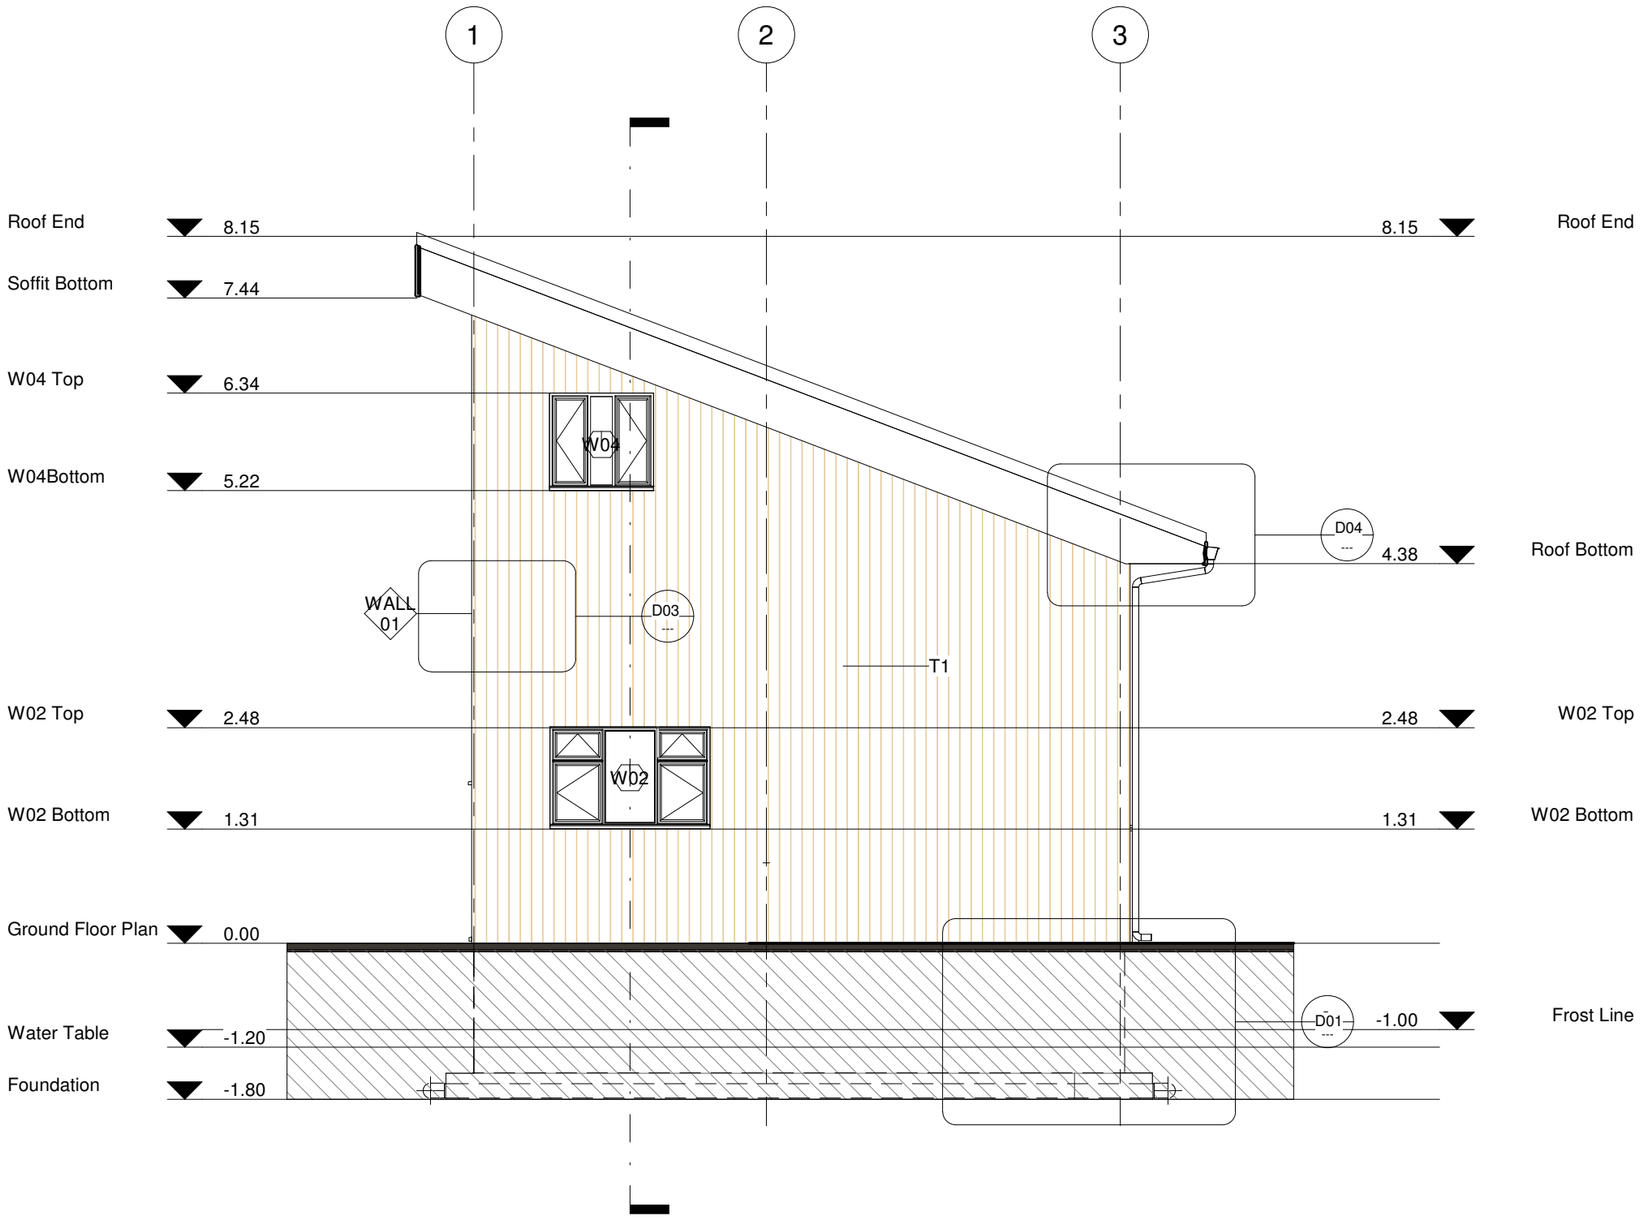


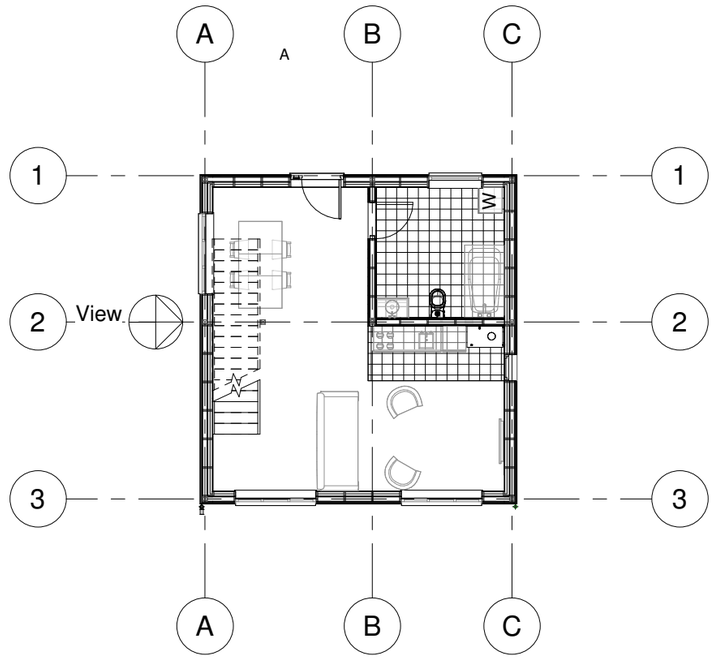

Key Plan

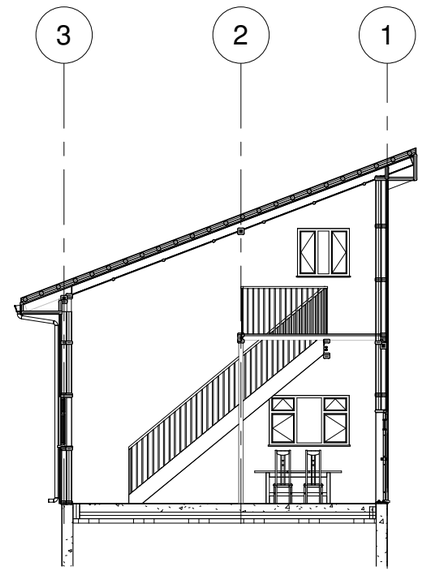

Key Section

WALL 01	
Gypsum wall board	1
Air	5.2
Rockwool insulation	5
OSB	1.5
Air infiltration barrier	0.2
Rockwool insulation	10
OSB	1.5
Breather membrane (Dupont Tyvek)	0.5
Waterproofing membrane	0.1
Battens	2.5
Timber cladding	1.7

T1: Timber cladding

N

TBM:938

M.E.T.U. FACULTY OF ARCHITECTURE DEPARTMENT OF ARCHITECTURE	ARCH351	BUILDING DETAIL MODELLING
	CHECKED BY:	
PORTFOLIO SUBMISSION		SCALE: 1/100
West Elevation Drawing		SHEET: A3
DRAWING BY: CİHAN AY-CİHAT İLKBAHAR		FINAL Submission
		DATE: 30.01.2022