

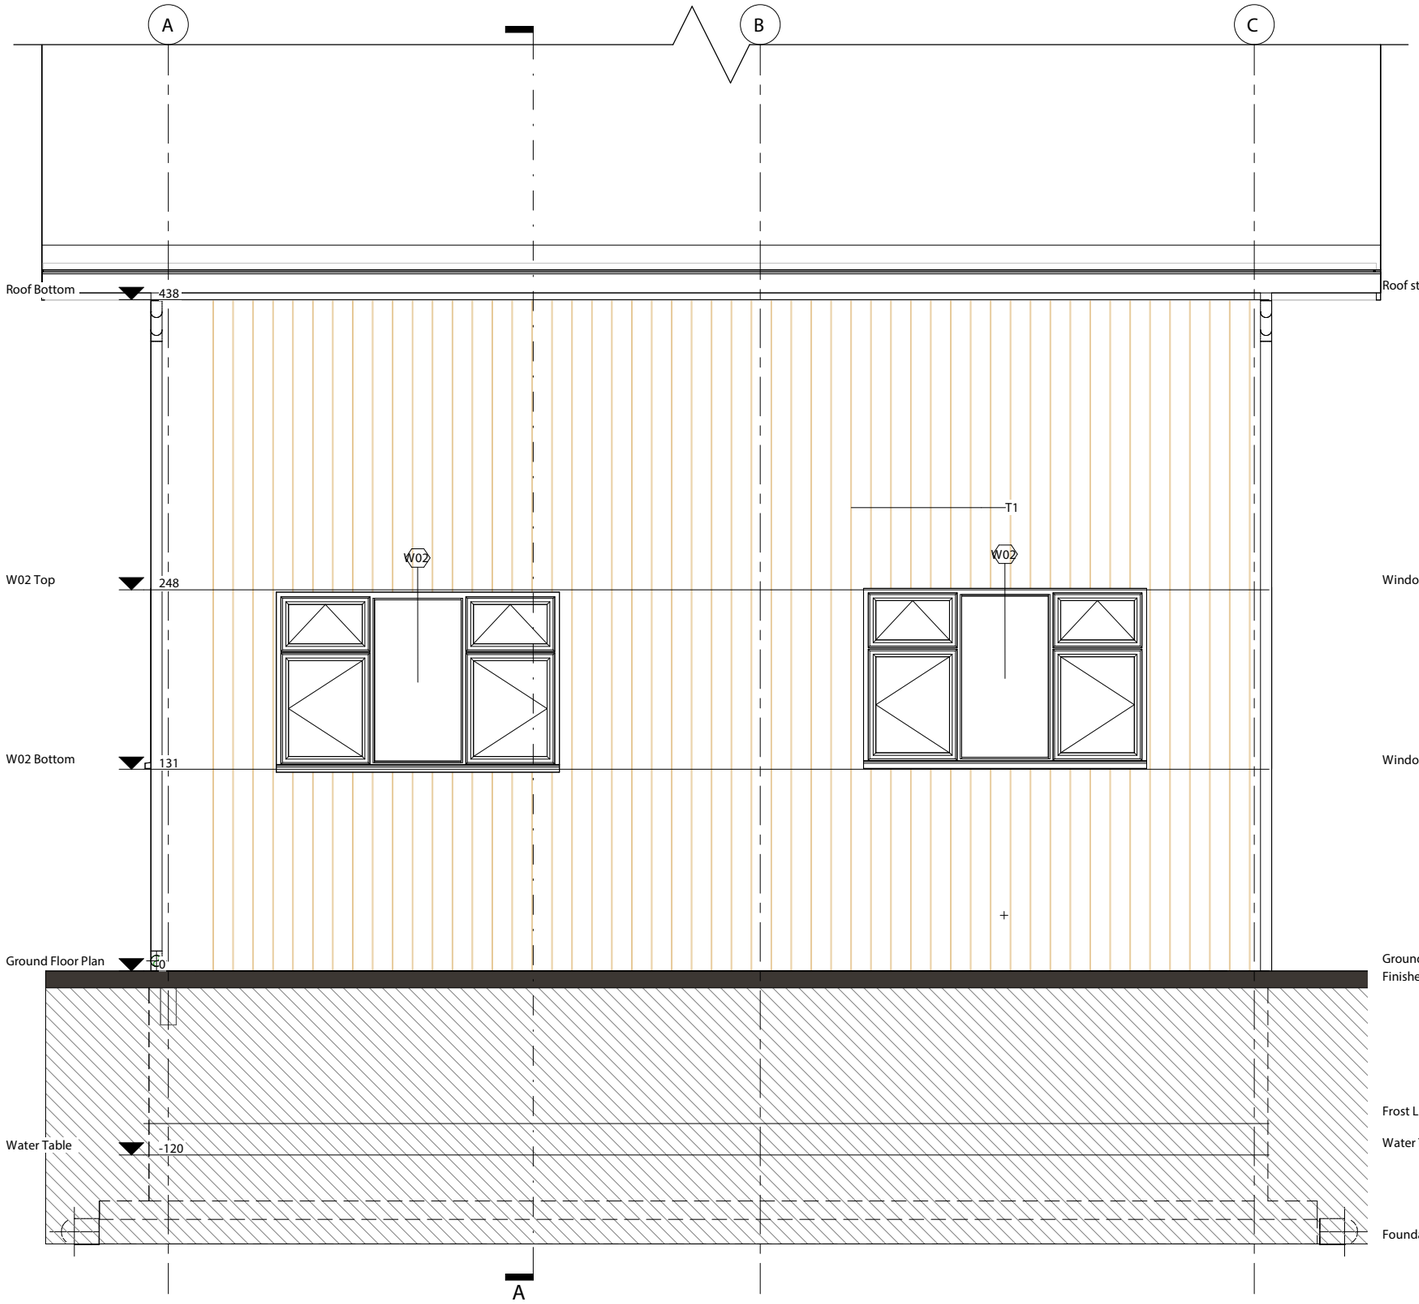


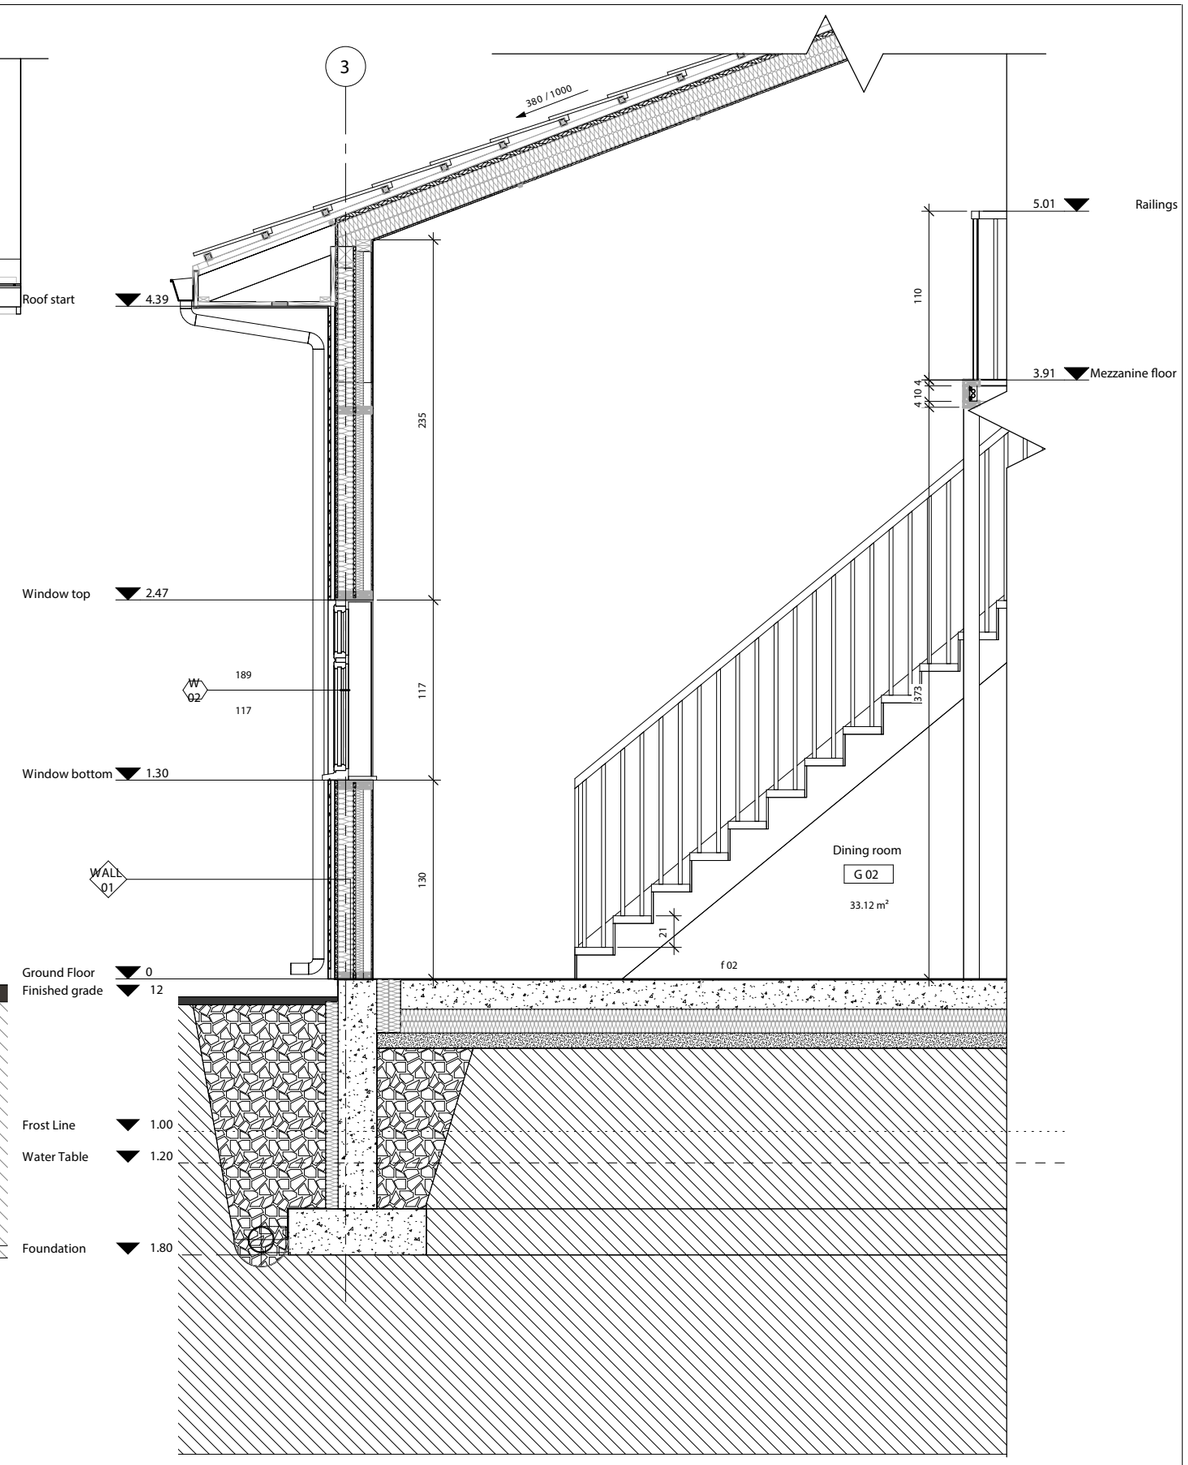

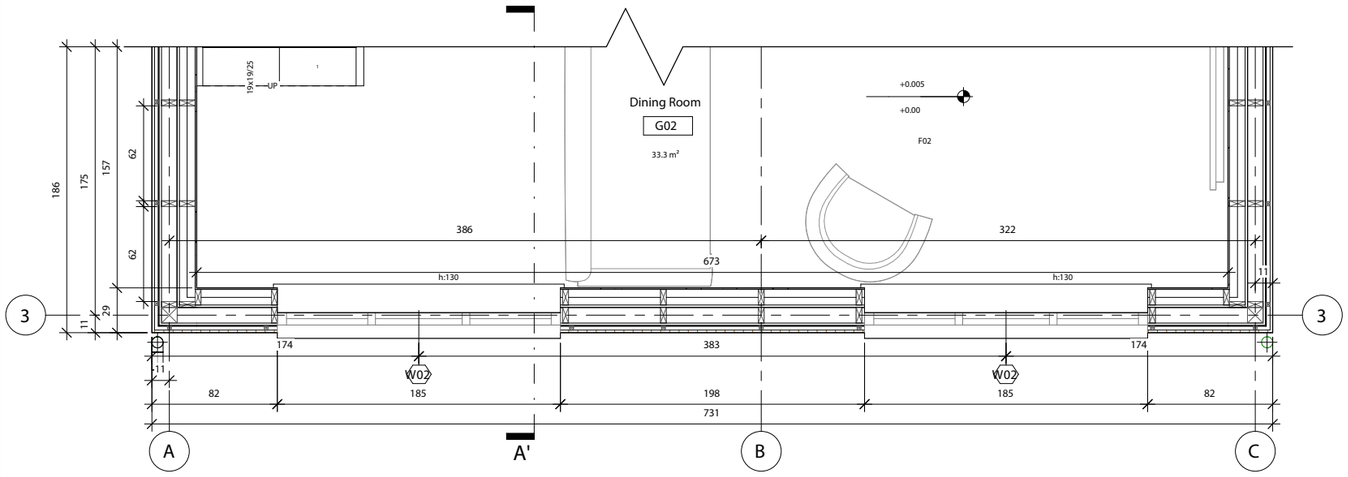

M.E.T.U. FACULTY OF ARCHITECTURE DEPARTMENT OF ARCHITECTURE	ARCH351	BUILDING DETAIL MODELLING
	CHECKED BY:	
PORTFOLIO SUBMISSION		SCALE: 1/40
SYSTEM SECTION		SHEET: A3
		FINAL EXAM
DRAWING BY: CİHAN AY - CİHAT İLKBAHAR		DATE: 30.01.2022