

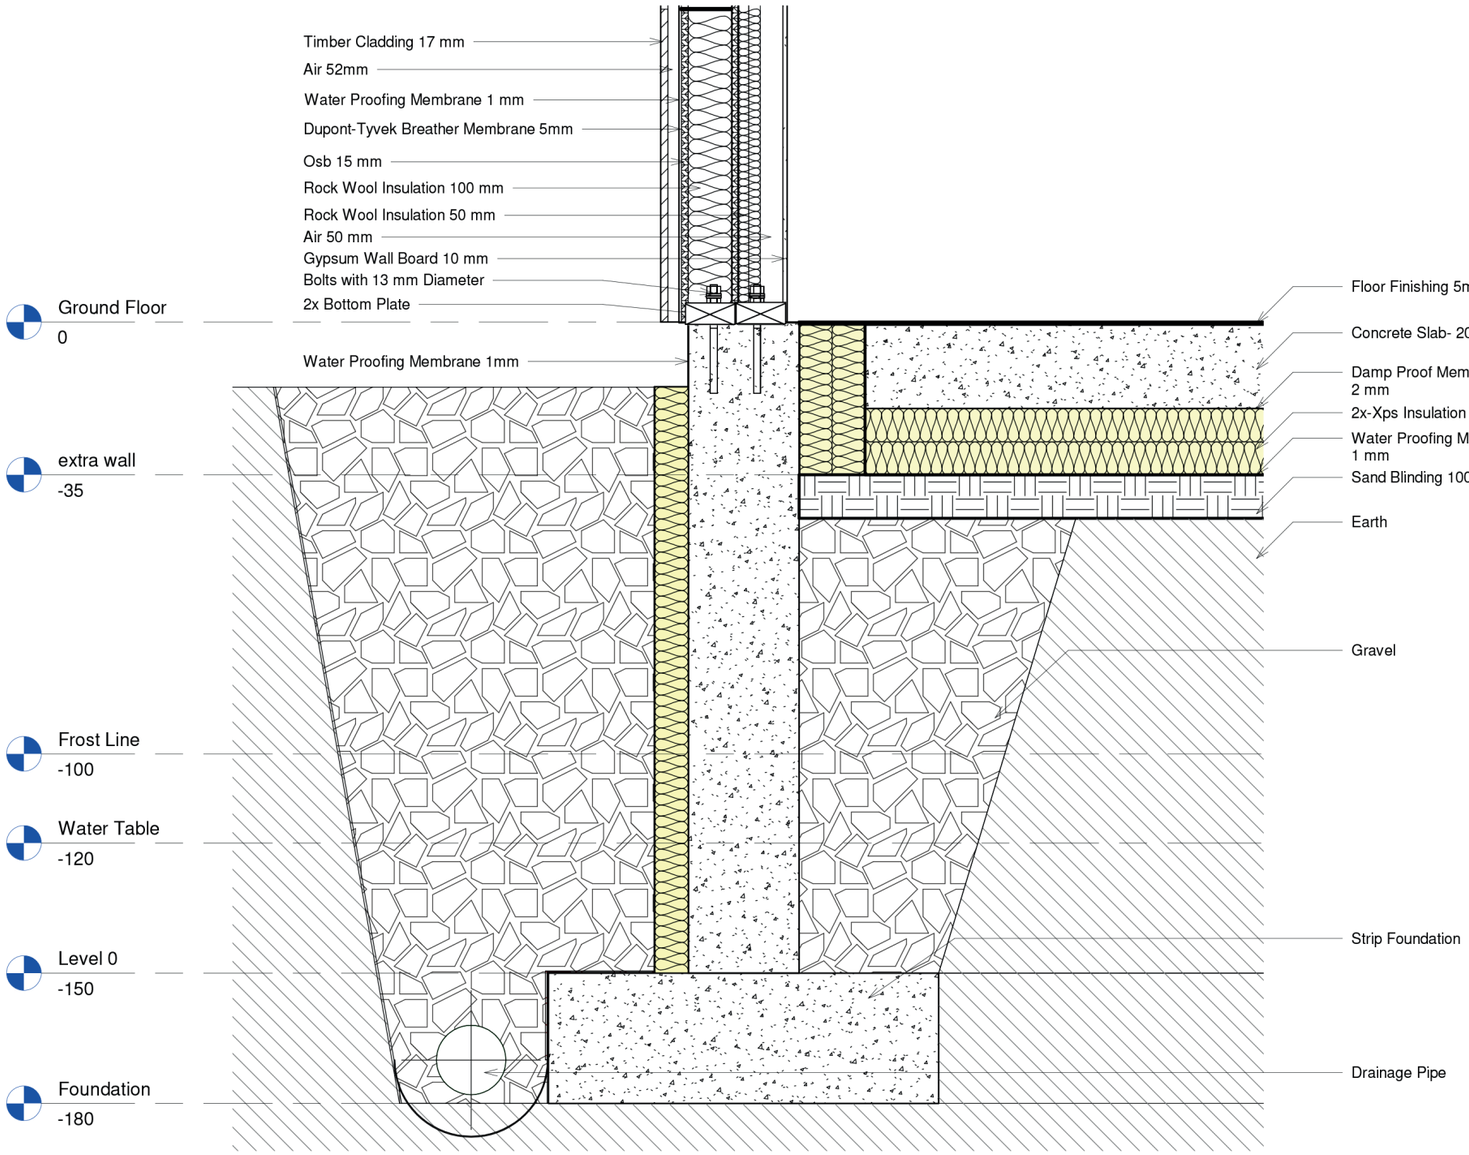


1 foundation wall-Floor detail

1 : 10

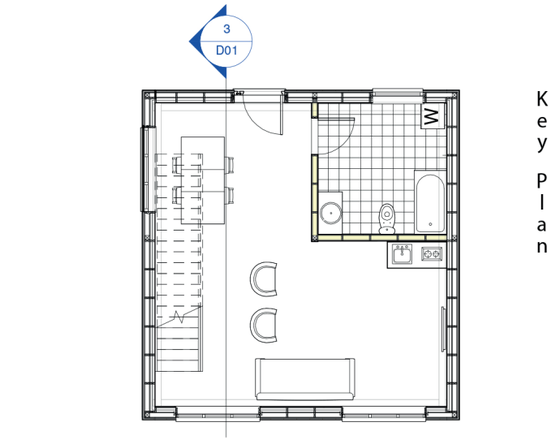

Key Plan

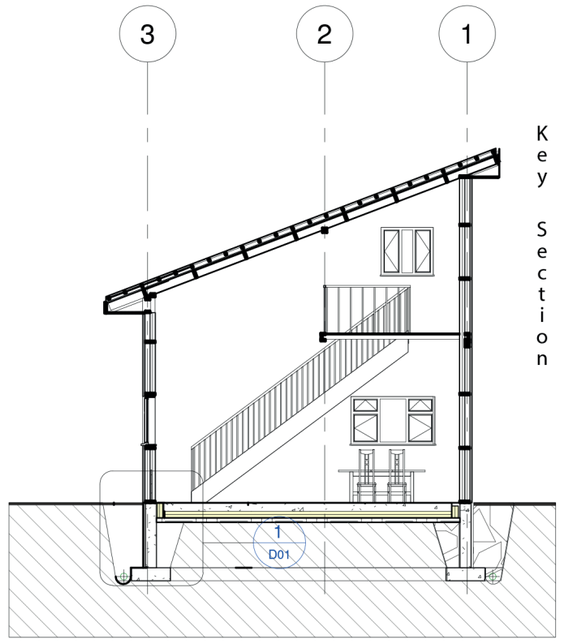

Key Section

TBM = 938

N

M.E.T.U. FACULTY OF ARCHITECTURE DEPARTMENT OF ARCHITECTURE	ARCH351	BUILDING DETAIL MODELLING
	CHECKED BY:	
PORTFOLIO SUBMISSION		SCALE: 1/20
DETAIL 01		SHEET: A3
DRAWING BY: CİHAN AY - CİHAT İLKBAHAR		FINAL EXAM
		DATE: 30.01.2022